WELHAVENSGT. 18

INNREDE BOLIGER PÅ LOFT

TOP FLOOR A/S, OSCARS GATE 76, OSLO 2

5

FASADE MOT WELHAVENSGATE

TEGN.NR. 10 MÅL. 1:100 SIGN: PHL

DAG TVILDE, ARK. MNAL, FR. NANSENS PL. 6

WELHAVENSGT. 18

INNREDE BOLIGER PÅ LOFT

TOP FLOOR A/S, OSCARS GATE 76, OSLO 2

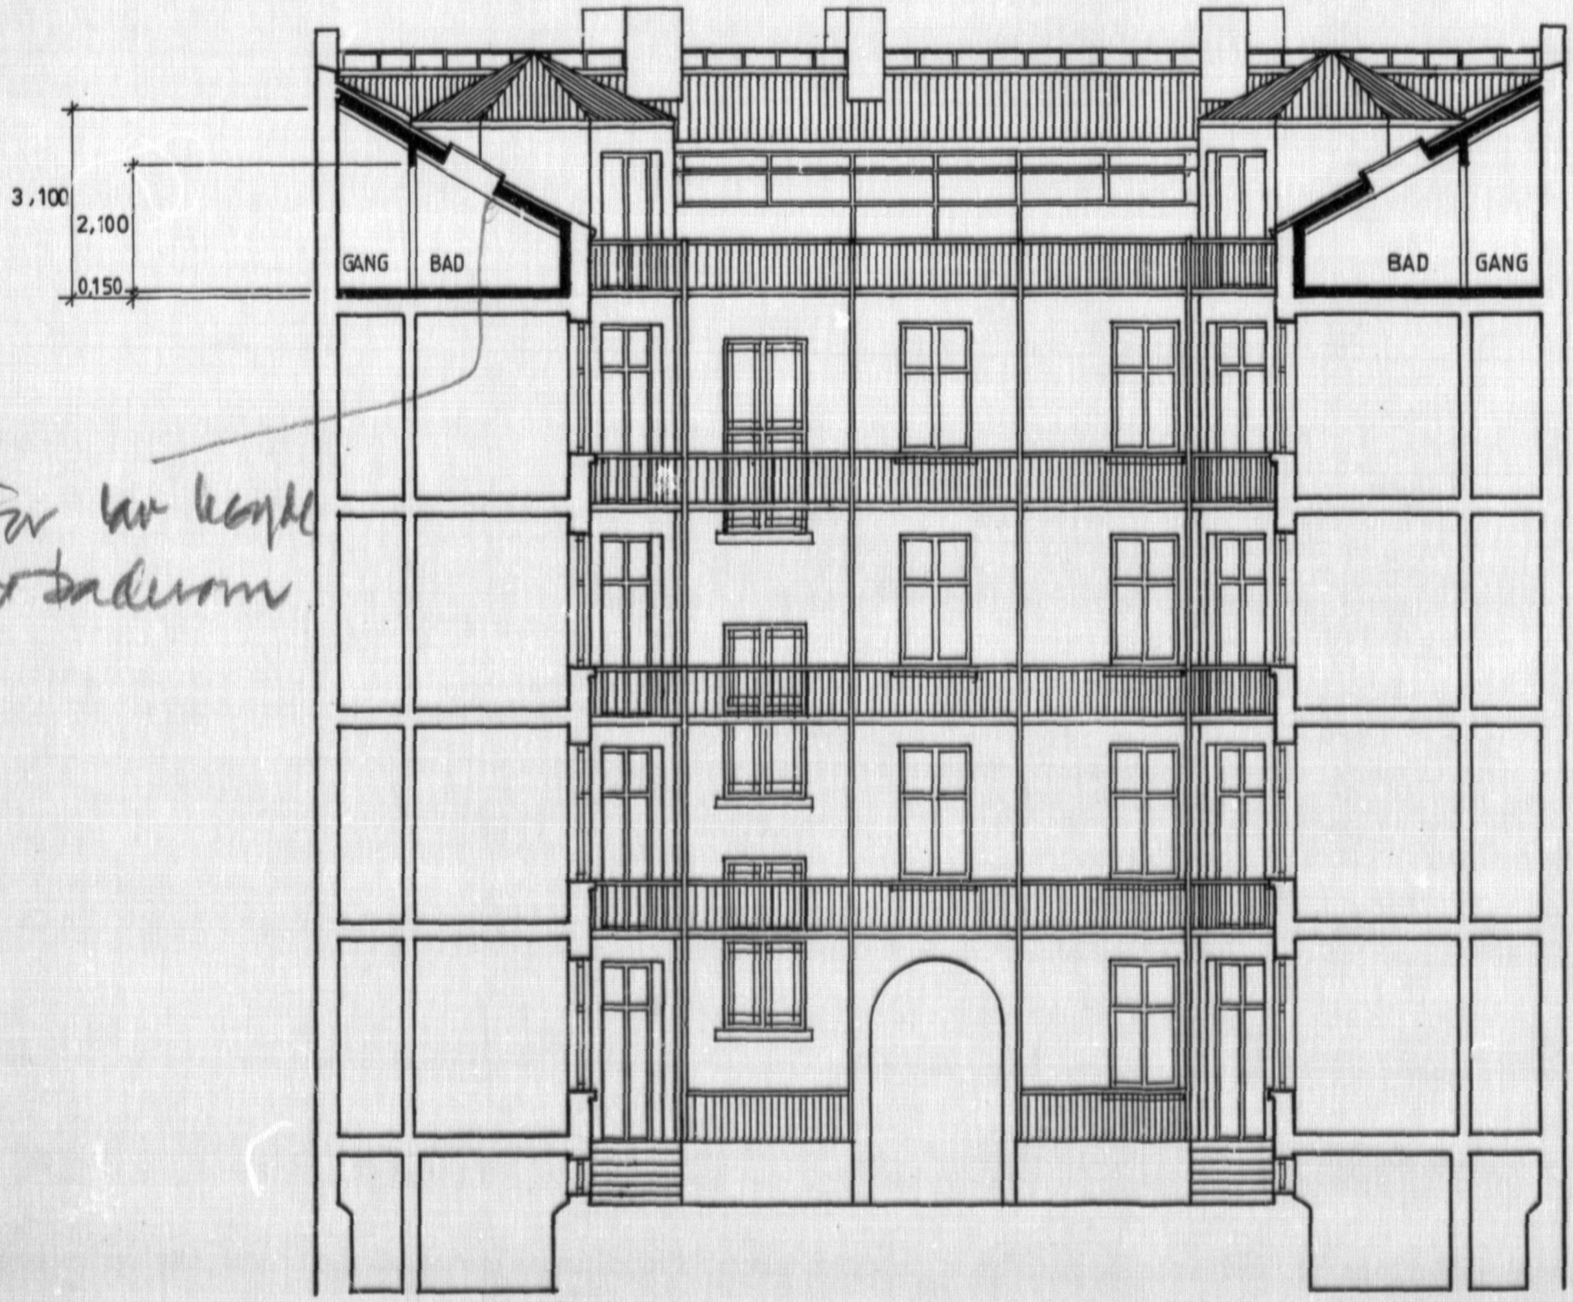

For lav kopfl
v baderom

6

FASADE GÅRDSROM / SNITT A-A

TEGN.NR. 11 MÅL 1:100 SIGN: TPL

DAG TVILDE, ARK. MNAL, FR. NANSENS PL. 6